

ARCHITECTURE PORTFOLIO



Agenda

2025

1/ Business
Hotel for 200
people

2/ Historic City
Apartment
Renovation

3/ Station for 400
passengers

4/ Private
Kindergarten
for 15 children

5/ Sixteen-story
building

6/ Tennis Club

7/ Apartment

8/ Village

9/ Apartment

10/ School





BUSINESS HOTEL FOR 200 PEOPLE





ABOUT THE PROJECT

Concept This project envisions a contemporary business hotel designed to accommodate 200 guests, combining functionality, comfort, and architectural clarity. The building features a clean geometric composition, a monochromatic black-and-white facade.

This project is more than just a building — it's a response to the needs of the contemporary city: how to create an environment where architecture serves people, not the other way around.




ARCHITECTURE

The complex consists of cascading volumes that integrate naturally into the terrain. Black and white facade modules create a rhythmic pattern that emphasizes the geometry of the structure, while large panoramic windows open the interior to the outside world. The contrast between the dark upper levels and the light base enhances visual dynamism.

01

The first floor serves as the central public hub of the hotel complex. It integrates guest reception, administrative services, and operational support zones. The layout is designed for smooth circulation, efficient logistics, and comfortable guest interaction.

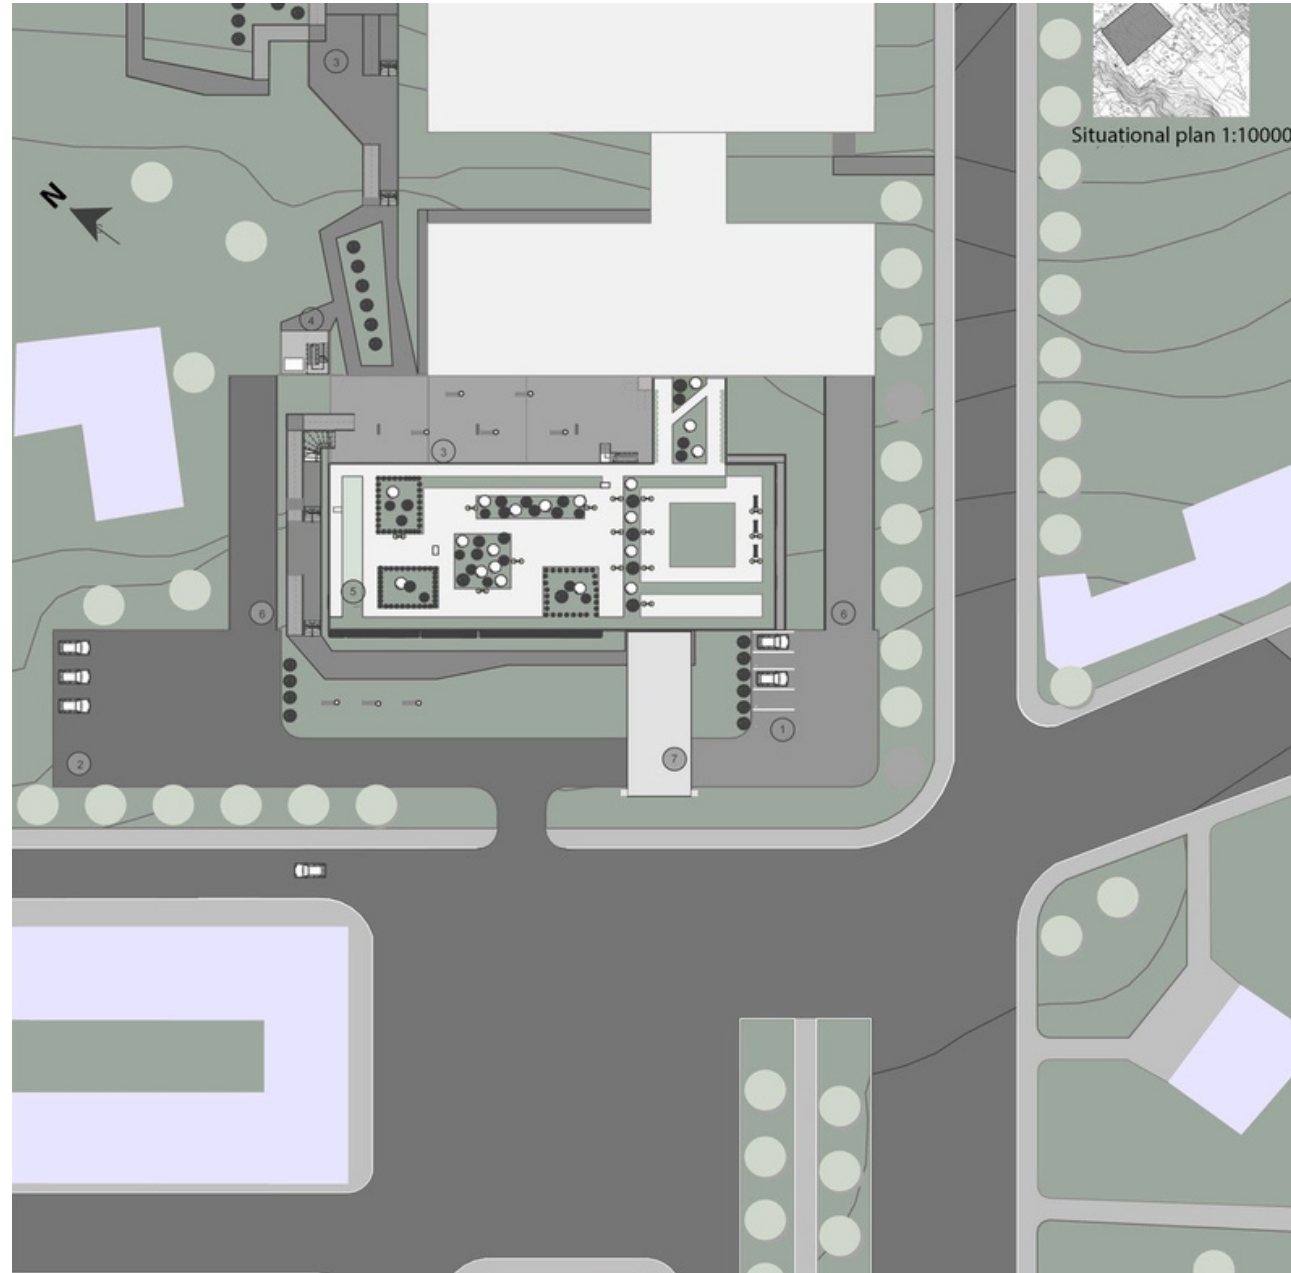


THE COMPLEX INCLUDES

- Temporary Parking for Visitors
- Staff Parking Area
- Walking Zone
- Exit from Underground Parking
- Rooftop Recreation Area (Third Floor, Block One)
- Entrance to Underground Parking
- Main Hotel Entrance


Ground floor plan explanation

1. Vestibule – 25 m²
2. Security Room – 11 m²
3. Lobby – 368 m²
4. Reception & Registration Office, Booking Office, Communication Point – 17 m²
5. Medical Room – 27 m²
6. Luggage Cart Storage – 10.5 m²
7. Duty Administrator's Room – 8 m²
8. Storage Room – 8 m²
9. Staff Duty Room – 7 m²
10. Safe Room – 6 m²
11. Accessible Room – 7 m²
12. Men's Restroom – 7.5 m²
13. Janitor's Closet – 1 m²
14. Women's Restroom – 7.5 m²
15. Cloakroom – 40 m²
16. Restaurant Hall – 293 m²
17. Restaurant Kitchen – 92 m²
18. Vegetable Storage – 8 m²
19. Dry Goods Storage – 8 m²
20. Container Storage – 8 m²
21. Meat Storage – 8 m²
22. Fish Storage – 8 m²
23. Bread Storage – 8 m²
24. Beverage Storage – 8 m²
25. Equipment Storage – 8 m²
26. Kitchenware Washing Room – 8 m²
27. Tableware Washing Room – 8 m²
28. Cleaning Supplies Storage – 8 m²
29. Staff Room – 8 m²
30. Staff Shower – 8 m²
31. Staff Restroom – 8 m²
32. Janitor's Closet – 1 m²
33. Security Room – 11 m²
34. Lobby – 368 m²
35. Reception & Registration Office, Booking Office, Communication Point – 17 m²
36. Medical Room – 27 m²
37. Vestibule – 25 m²
38. Restaurant Entrance – 5 m²
39. Hotel Entrance – 5 m²
40. Underground Parking – 388 m²

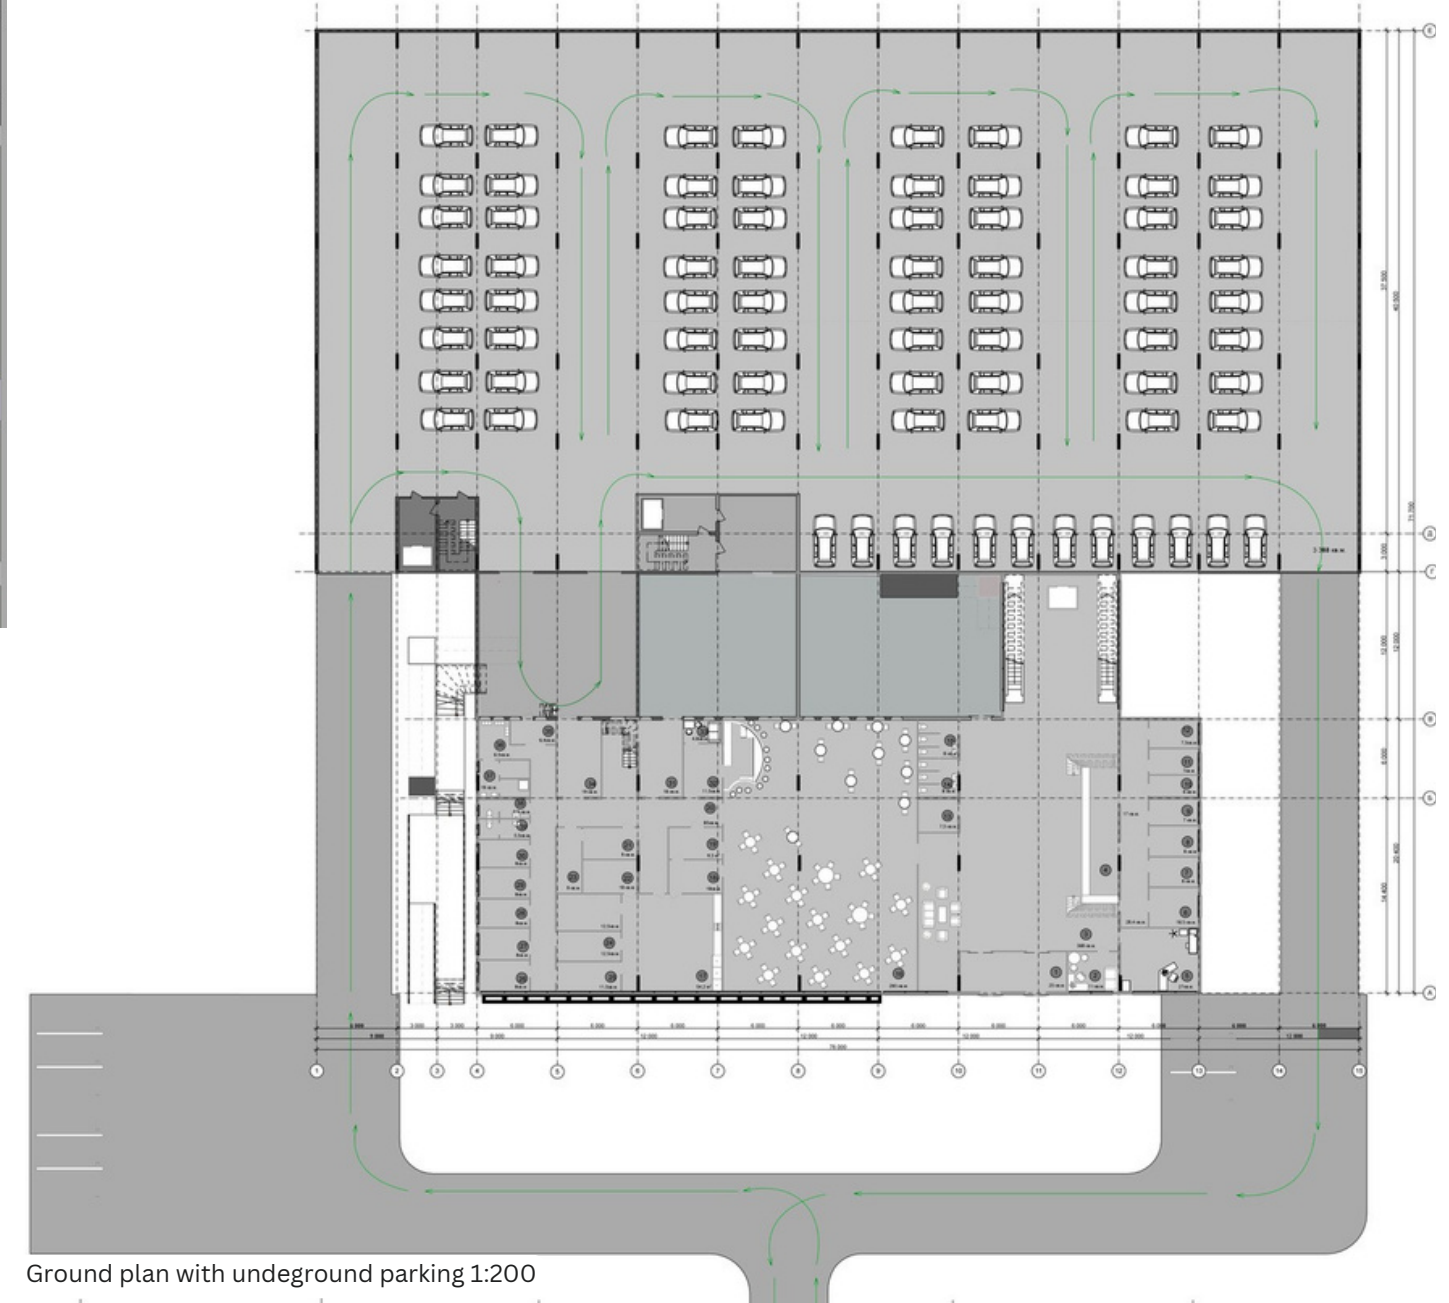


PLANS AND SECTIONS

02

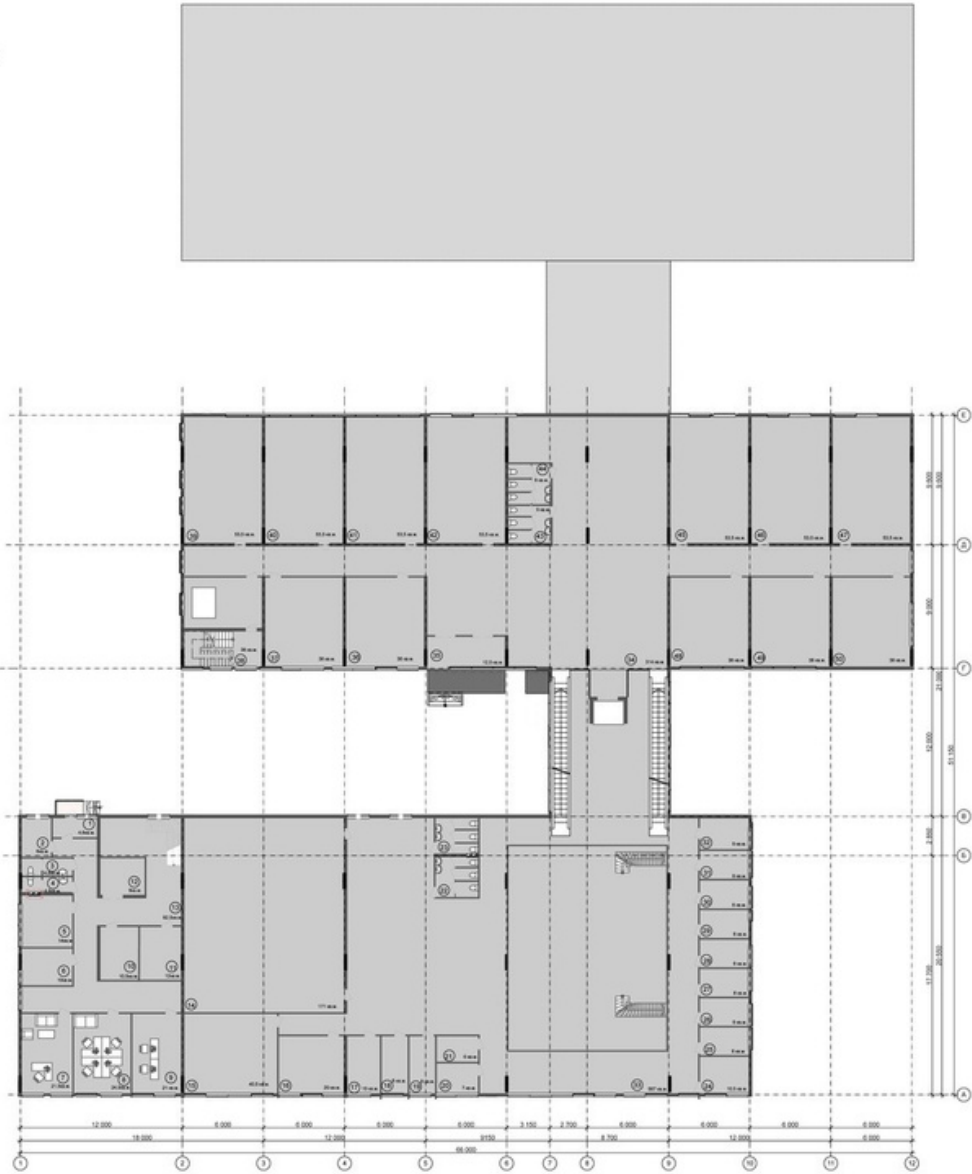



- First floor plan
- 1.Vestibule – 4.6 m²
 - 2.Cloakroom – 5 m²
 - 3.Men's WC – 4.8 m²
 - 4.Women's WC – 4.8 m²
 - 5.Dishwashing Room – 7 m²
 - 6.Director's Office – 21 m²
 - 7.Chief Accountant's Office – 21 m²
 - 8.Production Manager's Office – 21 m²
 - 9.Repair Room – 10 m²
 - 10.Storage Room – 9 m²
 - 11.Corridor – 82.5 m²
 - 12.Conference Hall – 38 m² 13-16. Accounting Office – 60 m² each
 - 13.Labor Department – 8 m²
 - 14.Men's WC – 7 m²
 - 15.Women's WC – 7 m²
 - 16.Storage Room – 6 m²
 - 17.Chief Engineer's Office – 21 m²
 - 18.Men's WC – 4.8 m²
 - 19.Women's WC – 4.8 m²
 - 20.Reception Room – 8 m² 25-26. Office – 21 m² each
 - 21.Chief Designer's Office – 21 m² 28-46. Office – 21 m² each
 - 22.Men's WC – 38 m²
 - 23.Women's WC – 38 m²
 - 24.Accessible WC – 38 m²
 - 25.Shop – 38 m²

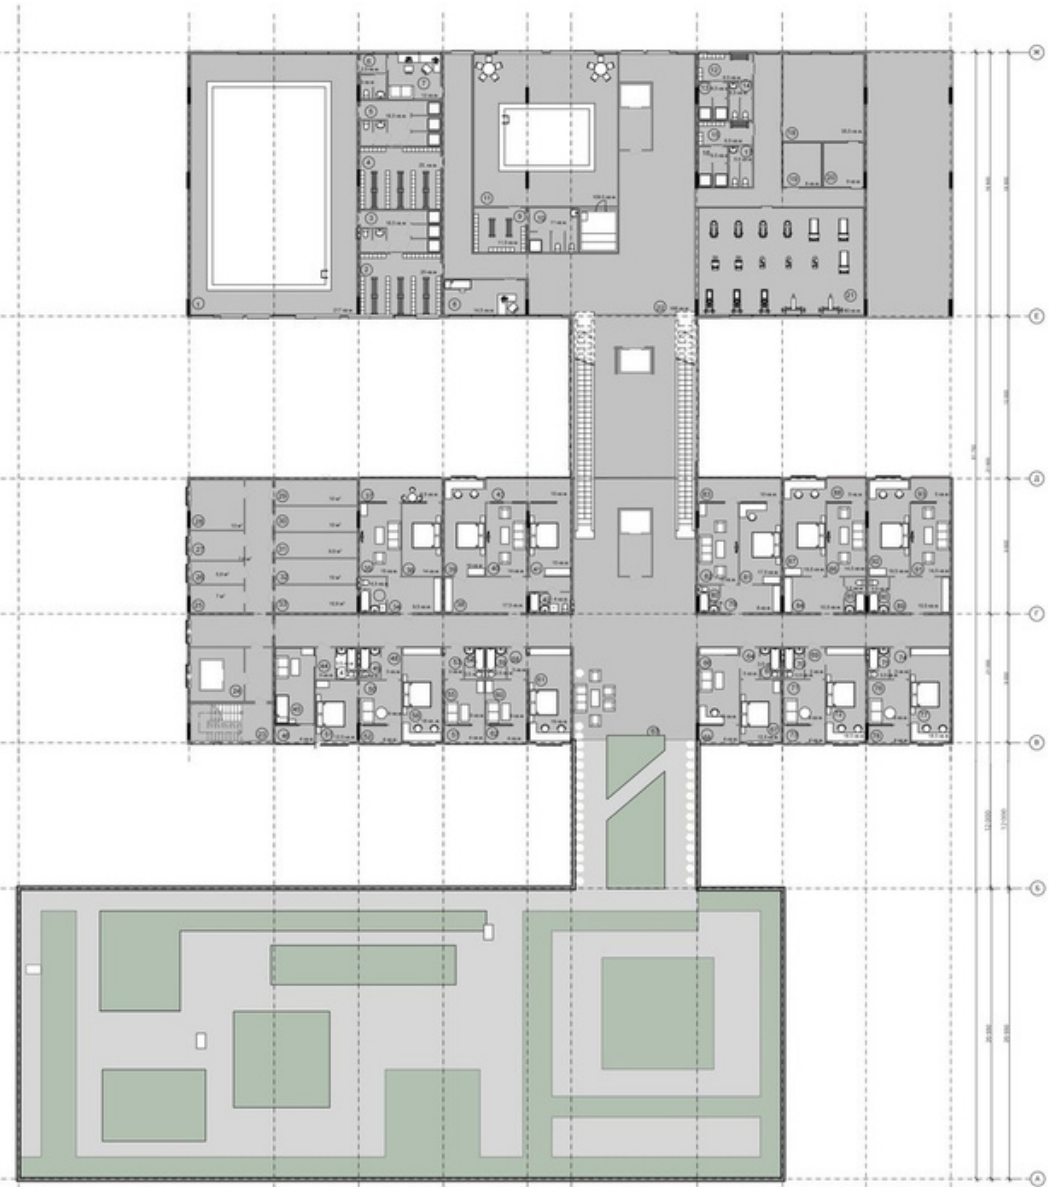

План третьего поверху М 1:200
Second floor plan 1:200

- Second floor plan
- 1.Swimming Pool – 217 m²
 - 2.Men's Changing Room – 25 m²
 - 3.Men's Showers – 18.5 m²
 - 4.Women's Changing Room – 25 m²
 - 5.Women's Showers – 18.5 m²
 - 6.Corridor – 2.5 m²
 - 7.Lobby – 9.5 m²
 - 8.Changing Room – 11.5 m²
 - 9.Shower + WC – 11 m²
 - 10.Sauna Pool – 109.5 m²
 - 11.Changing Room – 6.5 m²
 - 12.Women's Showers – 6.5 m²
 - 13.Men's Showers – 6.5 m²
 - 14.Women's Changing Room – 6.5 m²
 - 15.Men's Changing Room – 6.5 m²
 - 16. 16-19. Saunas – 6.5 m² each
 - 17. 20-23. Sauna Showers – 3 m² each
 - 18.Gym – 38 m²
 - 19.Gym Shower – 3 m²
 - 20.Gym WC – 3 m²
 - 21.Gym Changing Room – 6 m²

- Double Room (Total Area: 52 m²)
- Hall – 9.5 m²
 - Bathroom – 5 m²
 - Bedroom – 37.5 m²
- Double Room (Total Area: 79.5 m²)
- Hall – 9.5 m²
 - Bathroom – 5 m²
 - Bedroom – 65 m²

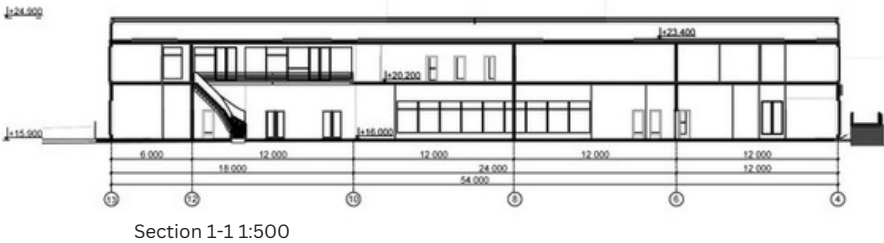
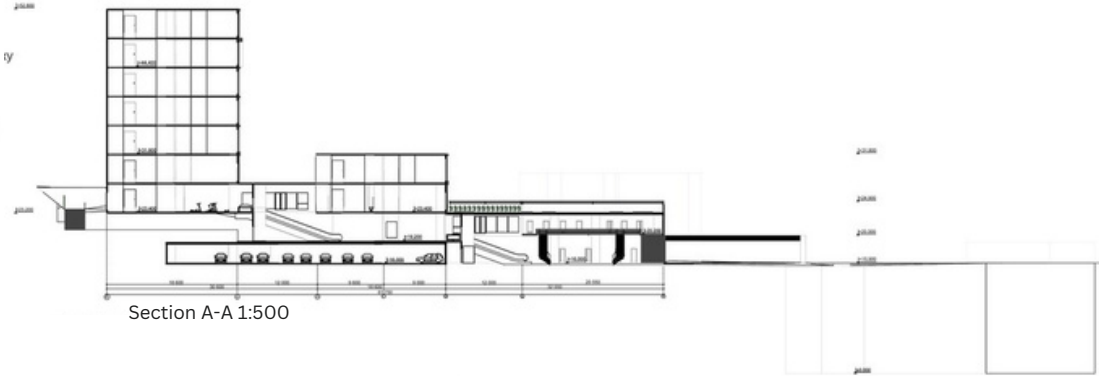


- One-room unit (1st category), total area: 25.5 m²
- Corridor – 3 m²
 - Bedroom – 15 m²
 - Balcony – 4 m²
 - Bathroom – 3.5 m²

- Two-room units, total area: 37.5-38.5 m²
- Corridor – 3 m²
 - Living Room – 9 m²
 - Bedroom – 18-19 m²
 - Balcony – 4 m²
 - Bathroom – 4 m²

- Junior Suite Studio
- Hall – 10.5 m²
 - Bathroom – 33.5 m²
 - Living Room – 14.5 m²
 - Bedroom – 19.5 m²
 - Balcony – 5 m²

- Two-room unit, total area: 52.5 m²
- Hall – 9.5 m²
 - Living Room – 15 m²
 - Bedroom – 21 m²
 - Balcony – 2.5 m²
 - Bathroom – 4.5 m²

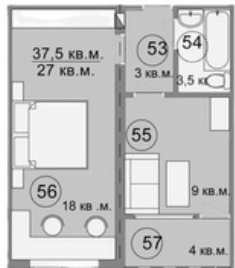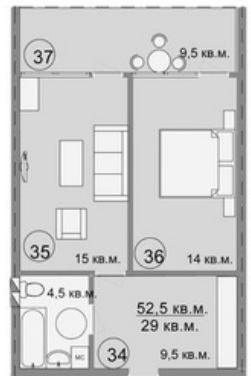



MY VISION

Spatial Composition

- Structure: Two-part volume — a two-story podium for public functions and a six-story tower for guest accommodations.
- Facade: Rhythmic arrangement of vertical and horizontal elements, large panoramic windows, and recessed balconies with metal railings.
- Materials: Composite panels, glass, and metal. Color palette: white, graphite, and black.

03

Landscape & Surroundings

- Greenery: Decorative trees, shrubs, ornamental grasses, and lawn zones.
- Pedestrian Areas: Paved walkways, benches, ambient lighting, and barrier-free access.
- Urban Integration: Strategically located near transport hubs and adjacent office buildings

05

Architectural Highlights

- Subtle evening illumination using warm LED fixtures to emphasize the building's geometry.
- Transparent ground floor design to foster openness and connection with the urban context.
- Harmonious contrast between the strict architectural lines and soft natural landscaping.

04

Building Program Overview

- | | |
|--|---|
| • Area: Reception & Lobby | • Area: Guest Rooms |
| • Floors: 1 | • Floors: 3–8 |
| • Description: Spacious entrance zone with lounge seating, waiting areas, and café | • Description: 200 rooms: standard, business, and executive suites. Some with balconies |
| • Area: Conference Facilities | • Area: Administrative Offices |
| • Floors: 1–2 | • Floors: 2 |
| • Description: Three flexible meeting rooms with movable partitions | • Description: Staff areas, technical rooms, and service corridors |
| • Area: Restaurant & Bar | • Area: Underground Parking |
| • Floors: 2 | • Floors: -1 |
| • Description: Panoramic windows, terrace access, open kitchen concept | • Description: 50-car capacity, separate access road |

06

HISTORIC CITY APARTMENT RENOVATION



Design created for living

The Art and Science of Design



Hanna Hovorukha project





Reconstruction Design

HISTORIC CITY APARTMENT RENOVATION

The project is located in a historic building in the city center. The task was to redesign and replan the space for a young couple.

Due to the wooden floor structure, there were restrictions on additional load. Therefore, laminate was chosen as the main flooring, while in the bathroom a minimal screed was applied and tiles were installed.



Entrance area

After replanning, the entrance area was redesigned with a built-in wardrobe. In the hallway, a niche was transformed into a console with a mirror that visually enlarges the space.

Modern minimalism

Modern minimalism is characterized by simplicity of forms, clean lines, and a limited number of decorative elements. The focus is on functionality, open spaces, and natural light. Materials and textures are used sparingly, often favoring natural or neutral tones. This style creates a sense of order, lightness, and contemporary elegance.

Open space

The apartment features an open, flowing layout, with the corridor seamlessly leading into the living room and kitchen. Decorative wooden slats define zones in the corridor, living room, and bedroom, adding rhythm and visual interest to the modern minimalist interior.

Living room

The living room is designed in a modern minimalist style with an open layout that flows seamlessly from the corridor and kitchen. The color palette echoes the kitchen and bedroom and is reflected in the textiles, creating a cohesive style. Decorative wooden slats define the lounge area, while a separate space is provided for entertaining guests, making the room both functional, cozy, and airy.

History of Life

Visualizations



The kitchen

The kitchen is compact yet fully functional, equipped with everything needed for daily cooking. The layout makes efficient use of space, and the windows offer beautiful views of the historic street.



The bathroom

The bathroom is designed to be highly functional and technically equipped, featuring shelves and niches for storage as well as a dedicated space for the washing machine. In the final realization, the flooring uses slightly different tiles than originally planned, but the overall concept of the space remains unchanged.



Home office

Functional home office with decorative panels as an accent. The space was redesigned: the piano area was replaced with a wardrobe, and the lounge furniture was moved against the wall. The office also has access to a balcony.




The bedroom

The bedroom is designed in a modern minimalist style, focusing on calmness and comfort. Colors and materials echo those used in other rooms, creating a harmonious space. Practical storage solutions are provided, and furniture placement ensures comfort and freedom of movement.

Bedroom view




The bedroom features a modern, minimalist design with a strong central axis defined by the bed and vertical wooden slat accent wall. A deep burgundy palette adds warmth and depth, while dark gray curtains introduce elegance and contrast. Floating nightstands and recessed lighting emphasize clean lines and spatial clarity. The built-in wardrobe integrates seamlessly into the architecture, with white upper panels that visually lift the ceiling. Overall, the space is balanced, functional, and visually refined.

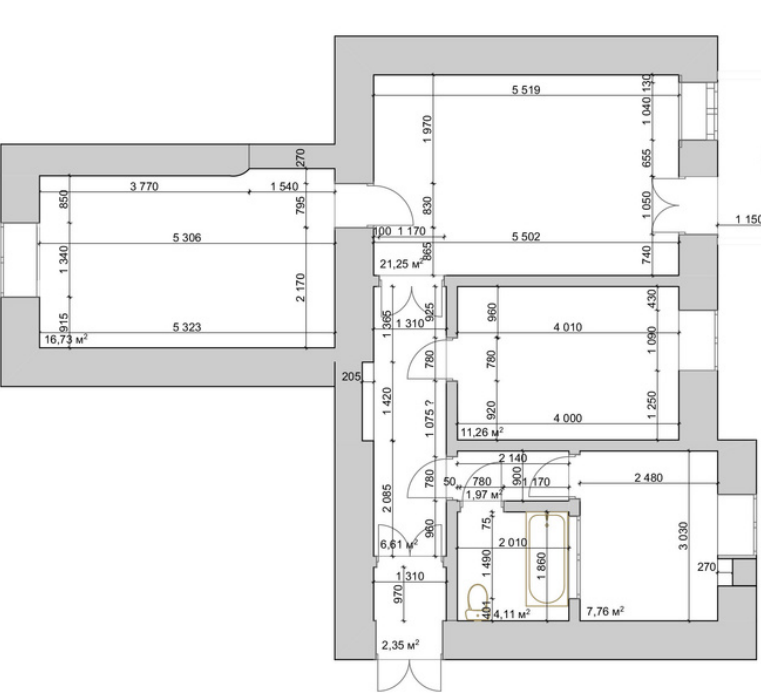




Measurement plan

The measured plan was created before the remodeling in scale 1:100. The drawing shows the actual condition of the space with all dimensions, load-bearing and non-load-bearing walls, door and window openings, as well as technical elements. This plan served as the basis for further design decisions.

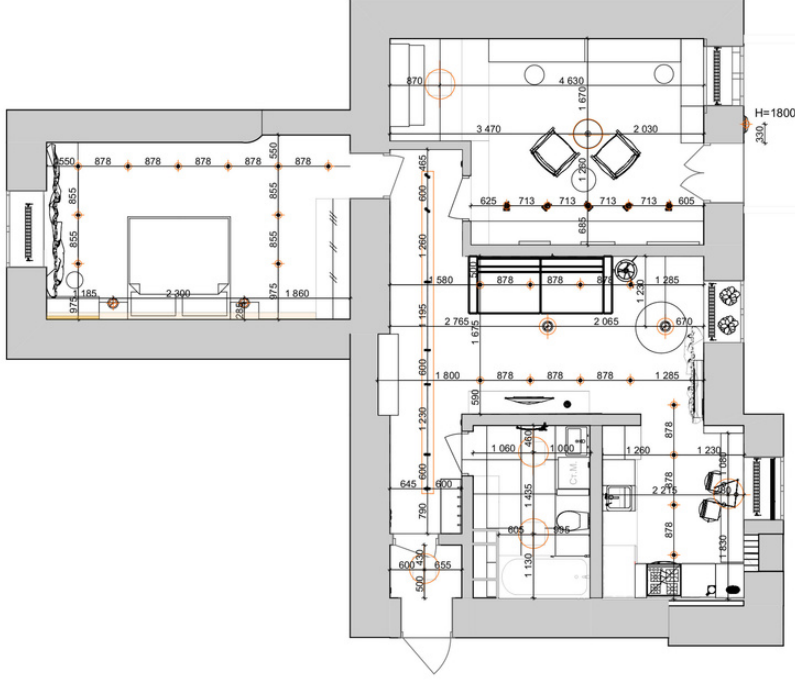


Lighting plan with furniture

The post-remodeling plan, drawn in scale 1:100, illustrates the updated layout with optimized space organization. It includes the arrangement of furniture and the lighting concept, highlighting both functional and aesthetic aspects of the design. This plan demonstrates the transformation of the apartment into a coherent and comfortable living environment.

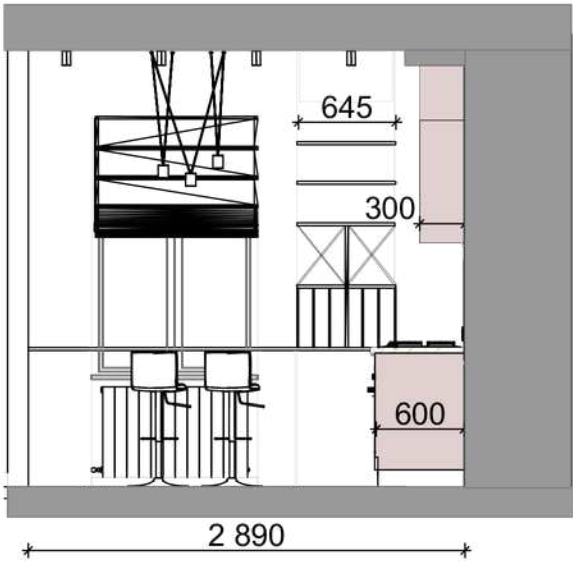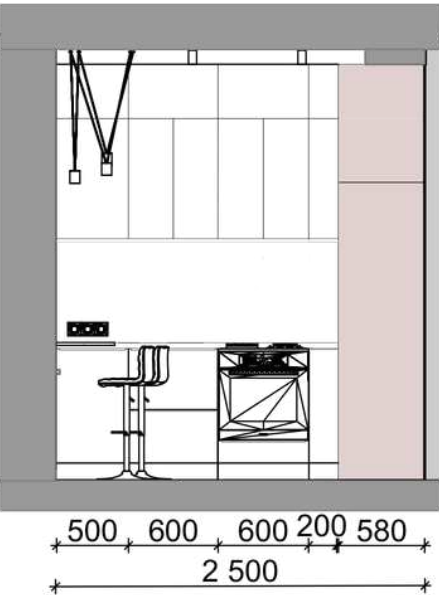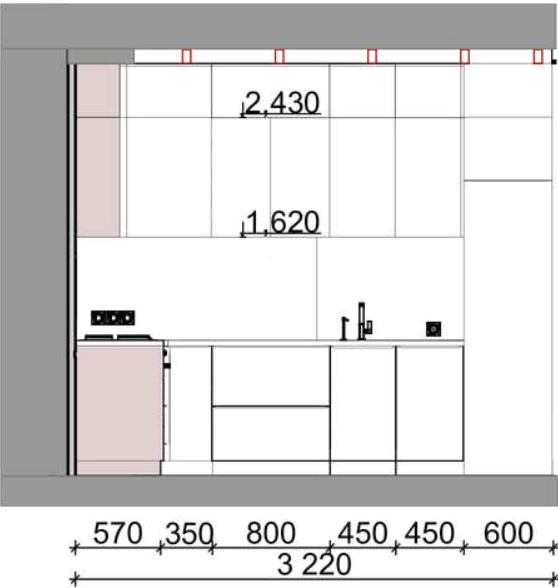

Kitchen sections

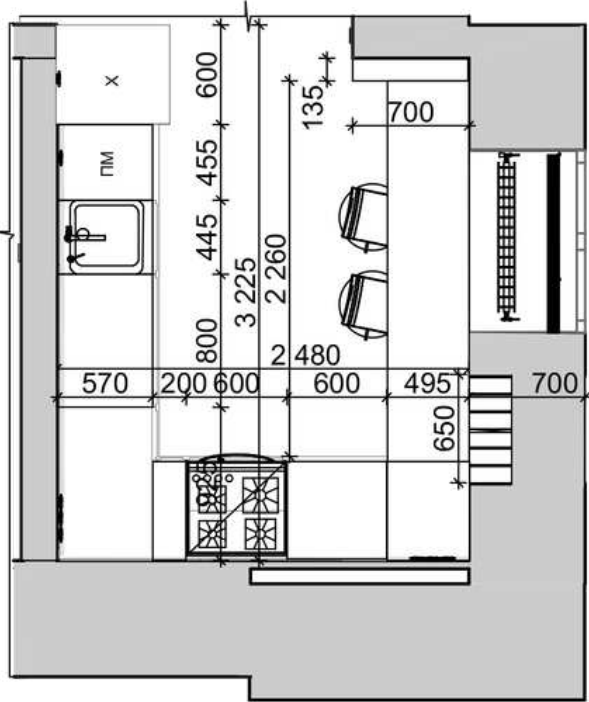

Kitchen plan 1:50



Hanna Hovorukha project



Urban Design

Real photo




STATION FOR 400
PASSENGERS






A bus terminal for 400 passengers includes a forecourt, a public transport stop nearby, a parking area, a boarding platform, a retail zone, and designated spaces for bus layover and maintenance.

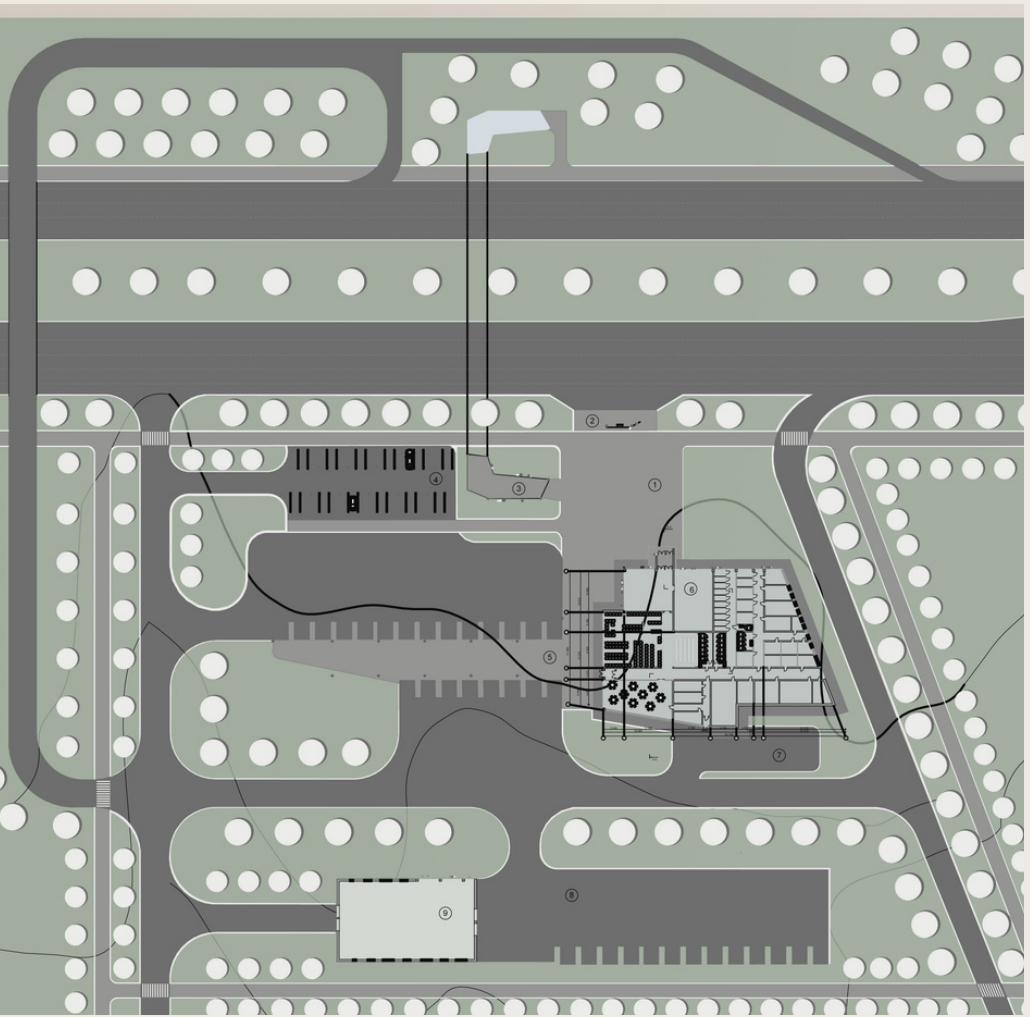

The bus terminal building is a single-story structure with a flat roof and a wide canopy above the entrance. The facade is made of glass and metal, providing transparency, natural lighting, and a contemporary appearance. The design is minimalist, with clear zoning and convenient navigation for passengers.

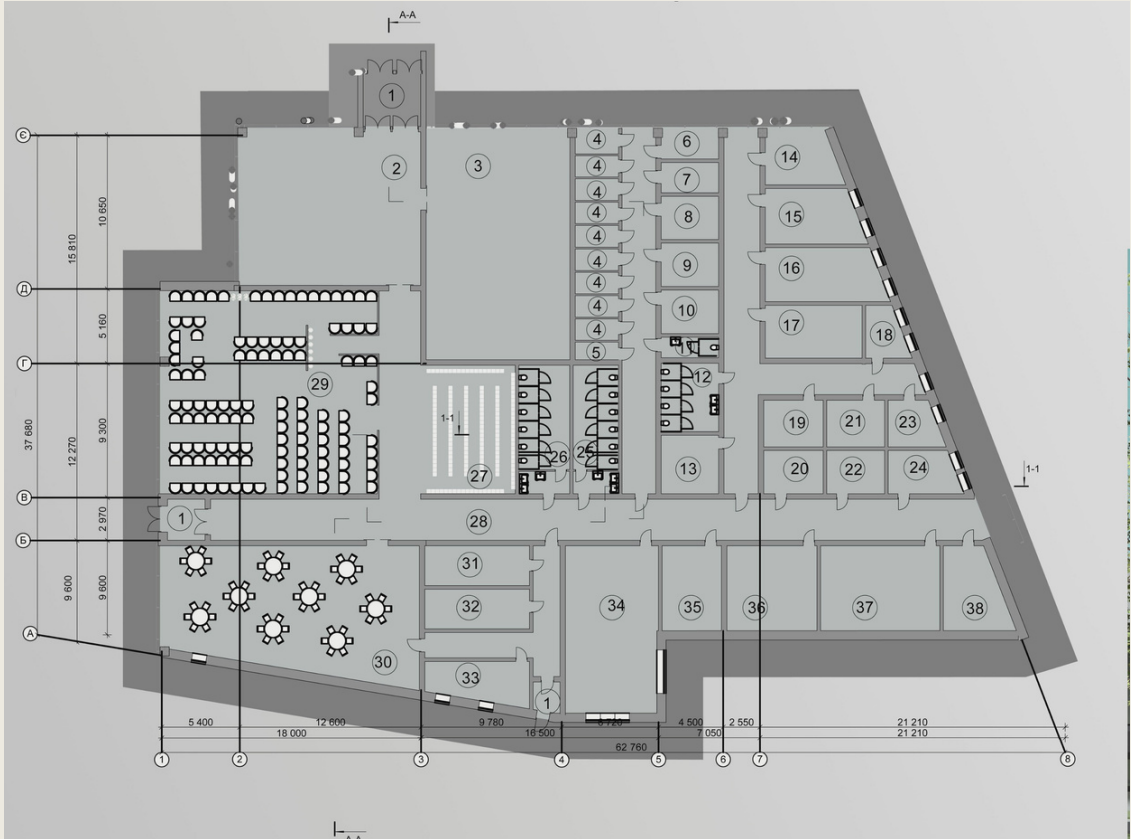


PRIVAT KINDERGARTEN FOR 15 CHILDREN



Mood Visualization




Apartment Conversion into a Private Kindergarten

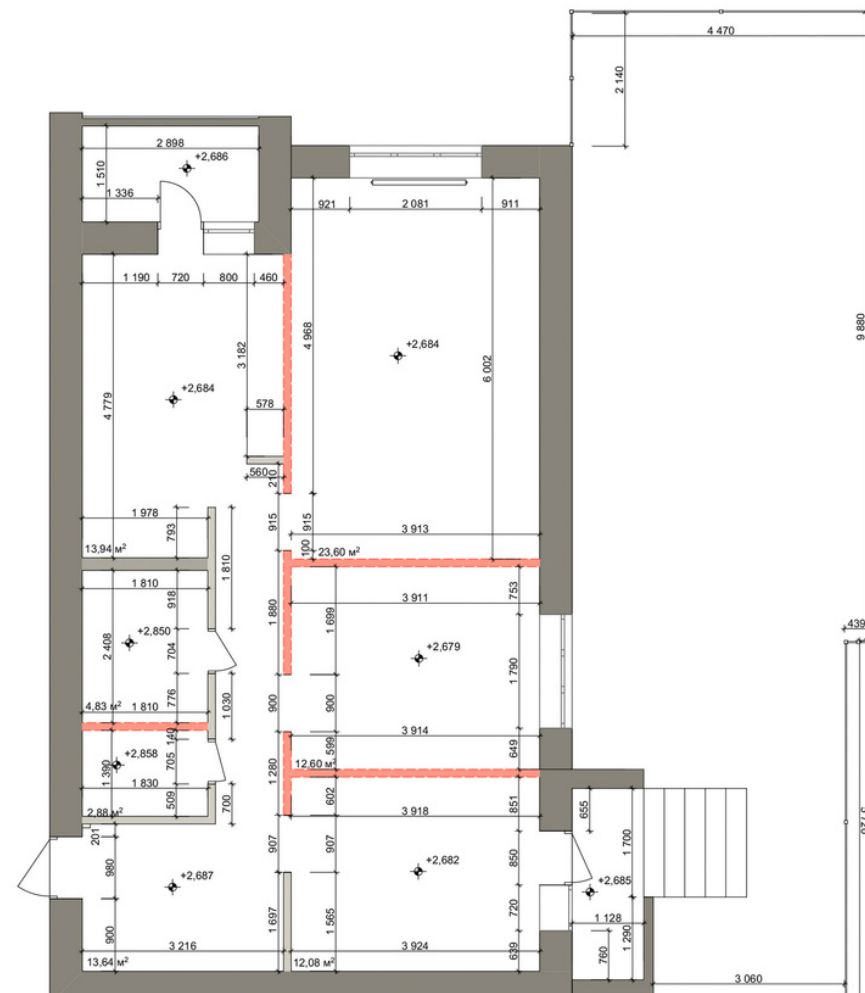

Demolition plan 1:100


This project involved converting an apartment with a small courtyard into a private kindergarten.

The apartment has two separate entrances, which proved to be a great advantage for organizing the layout.

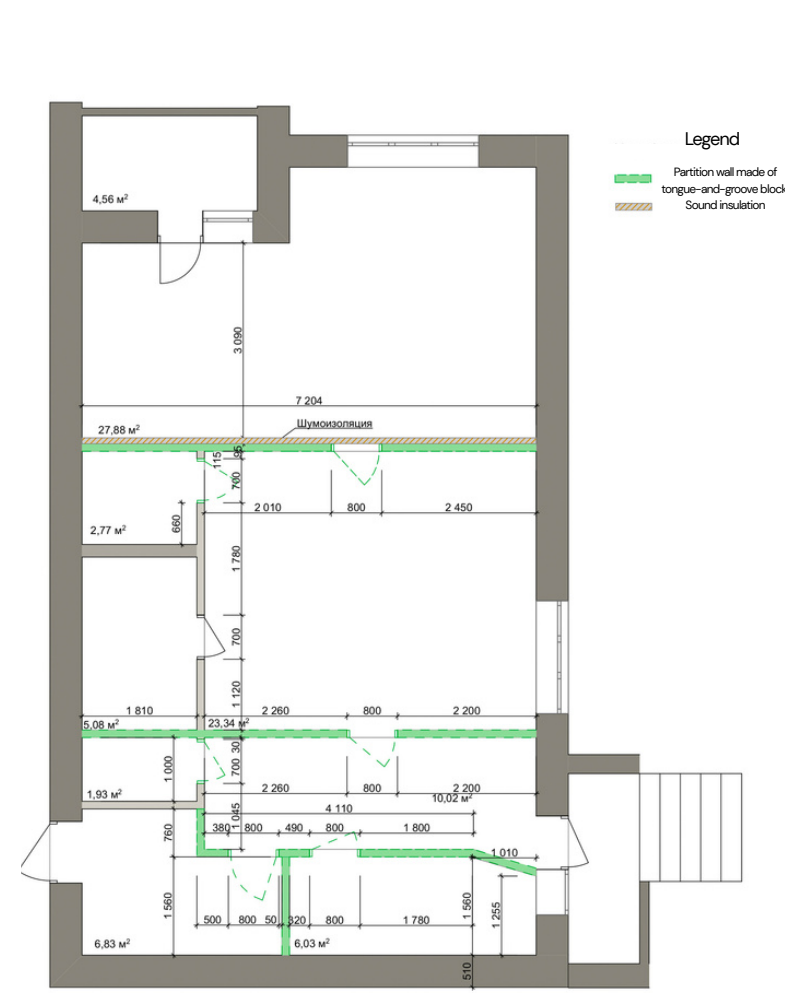


Installation plan 1:100

On one side, a reception area was placed, and the kitchen was redesigned and slightly reduced in size but kept fully functional, allowing for food preparation, reheating, washing, and storage. A corridor with lockers connects the entrance area to the main space and leads to an adult restroom for staff and visitors.

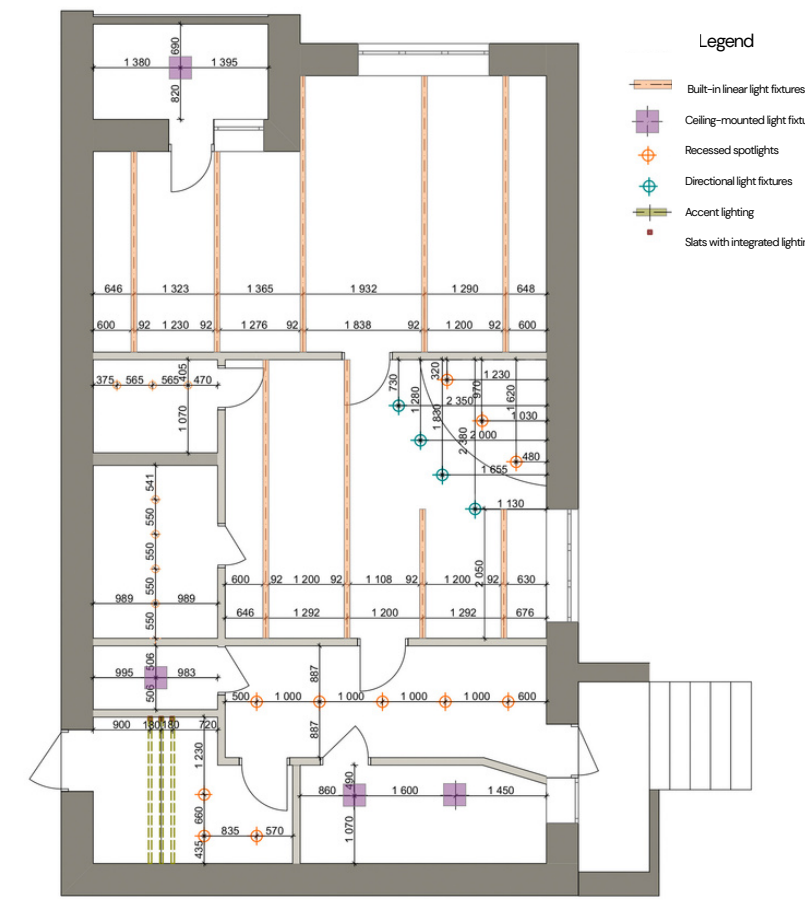

Lighting plan 1:100

The heart of the project is the play and dining area, which also includes a projector and a small stage for children's performances. From here, there is access to the children's restroom and a technical room with a laundry area. The play/sleep room features transformable beds, allowing the space to adapt easily to different activities.

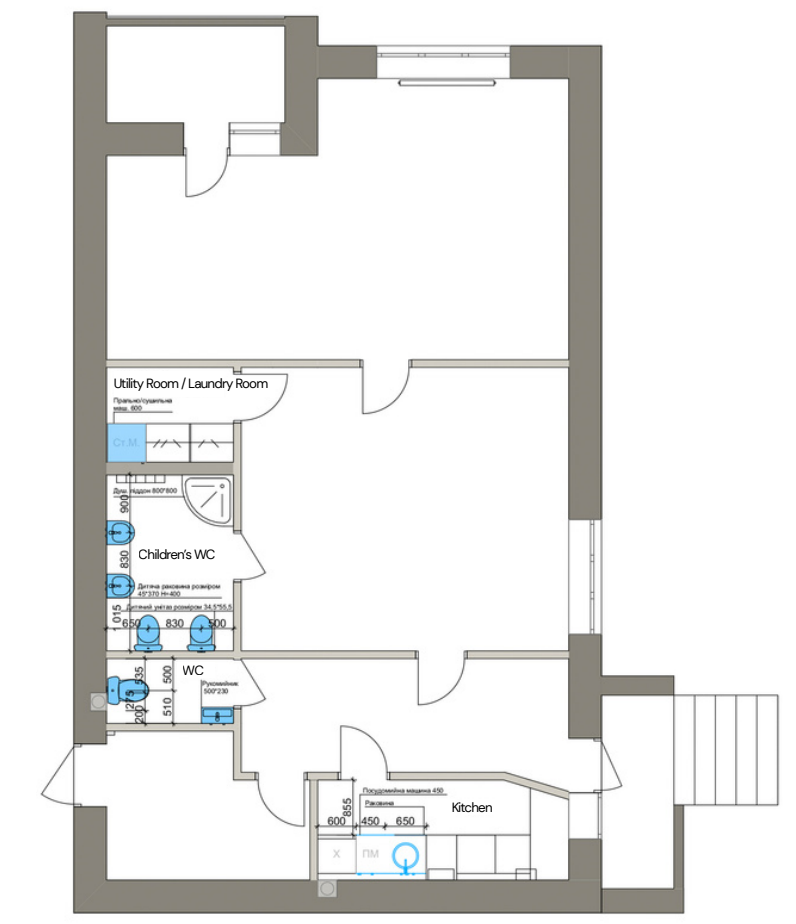

Plumbing plan 1:100

A small office is located on the balcony for administrative work. Outside, on the private courtyard, there is a play area where children can safely enjoy outdoor activities. It was also recommended to install ceiling sound insulation and add extra soundproofing for the laundry area to reduce noise from equipment.




General View of the Project



SIXTEEN-STORY BUILDING




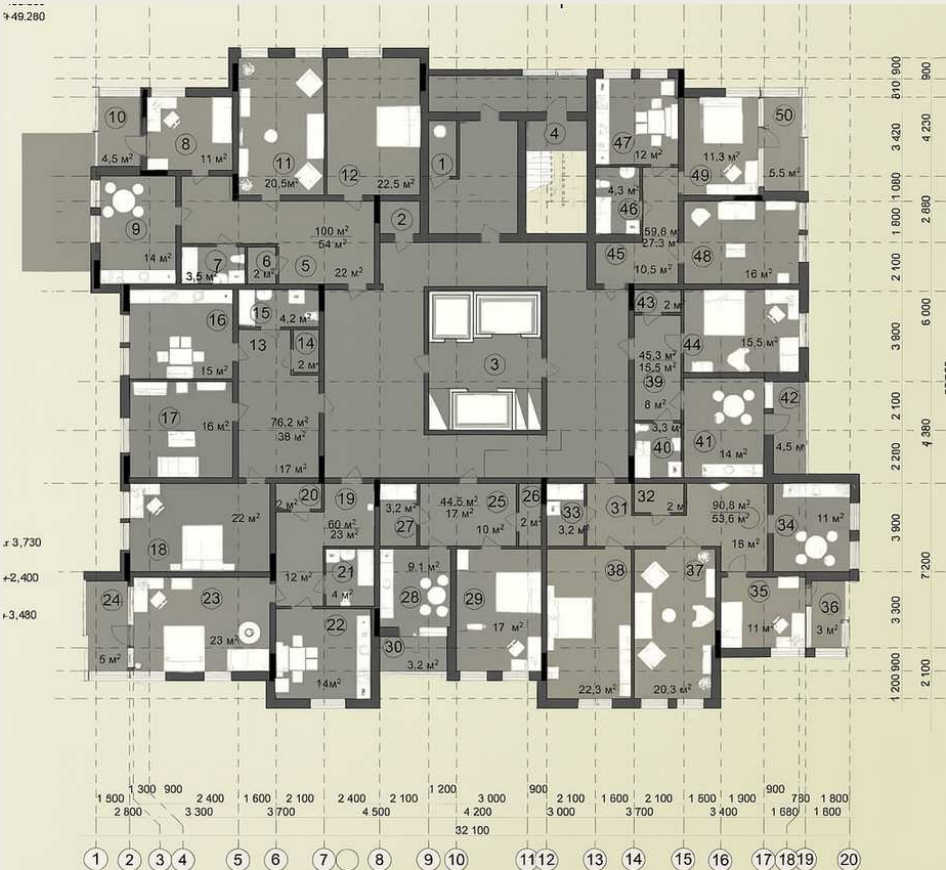

Vertical” is a modern residential development designed for urban living. The building features a variety of apartment layouts to accommodate different lifestyles, complemented by underground parking and landscaped outdoor areas. Color accents are applied to entrance doors, selected facade volumes, and anti-trauma flooring in shared zones, adding vibrancy and identity. The project includes safe children’s playgrounds and integrates greenery and pedestrian paths to create a welcoming and functional environment.

TENNIS CLUB



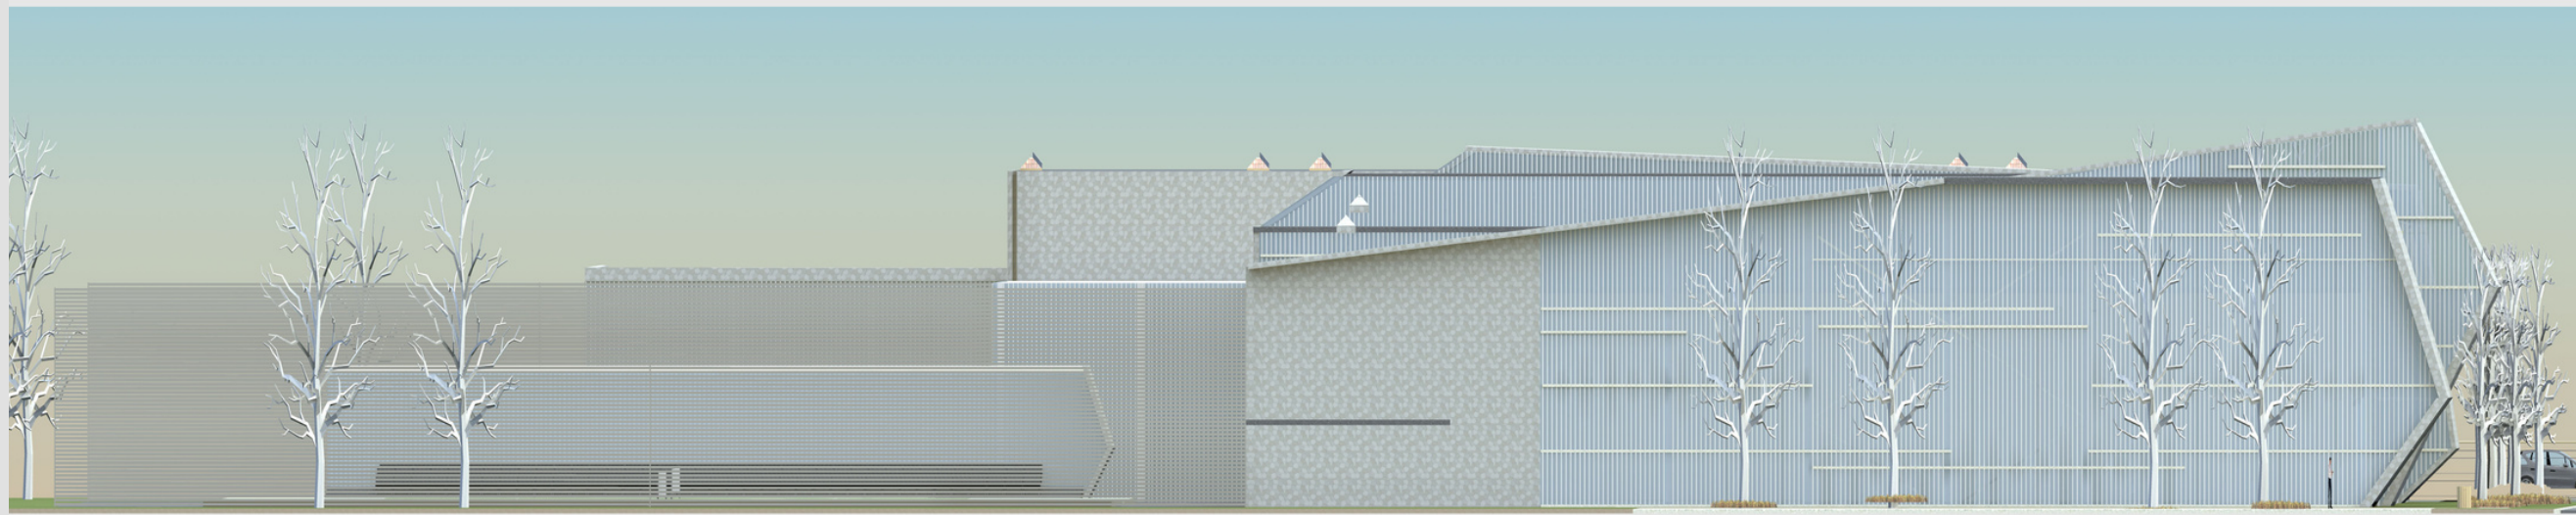


Tennis Club

Architectural Concept

The Tennis Club is a dynamic sports facility that blends geometric clarity with functional zoning. The complex consists of angular volumes arranged along the main street, forming an open, accessible, and visually striking structure.

- Facade: a mix of dark and light panels, glass inserts, and metal accents.
- Landscape: greenery, pedestrian paths, parking, and lighting integrated into the urban context.
- Spatial layout: clearly defined zones — training halls, administrative offices, relaxation areas, café, locker rooms.



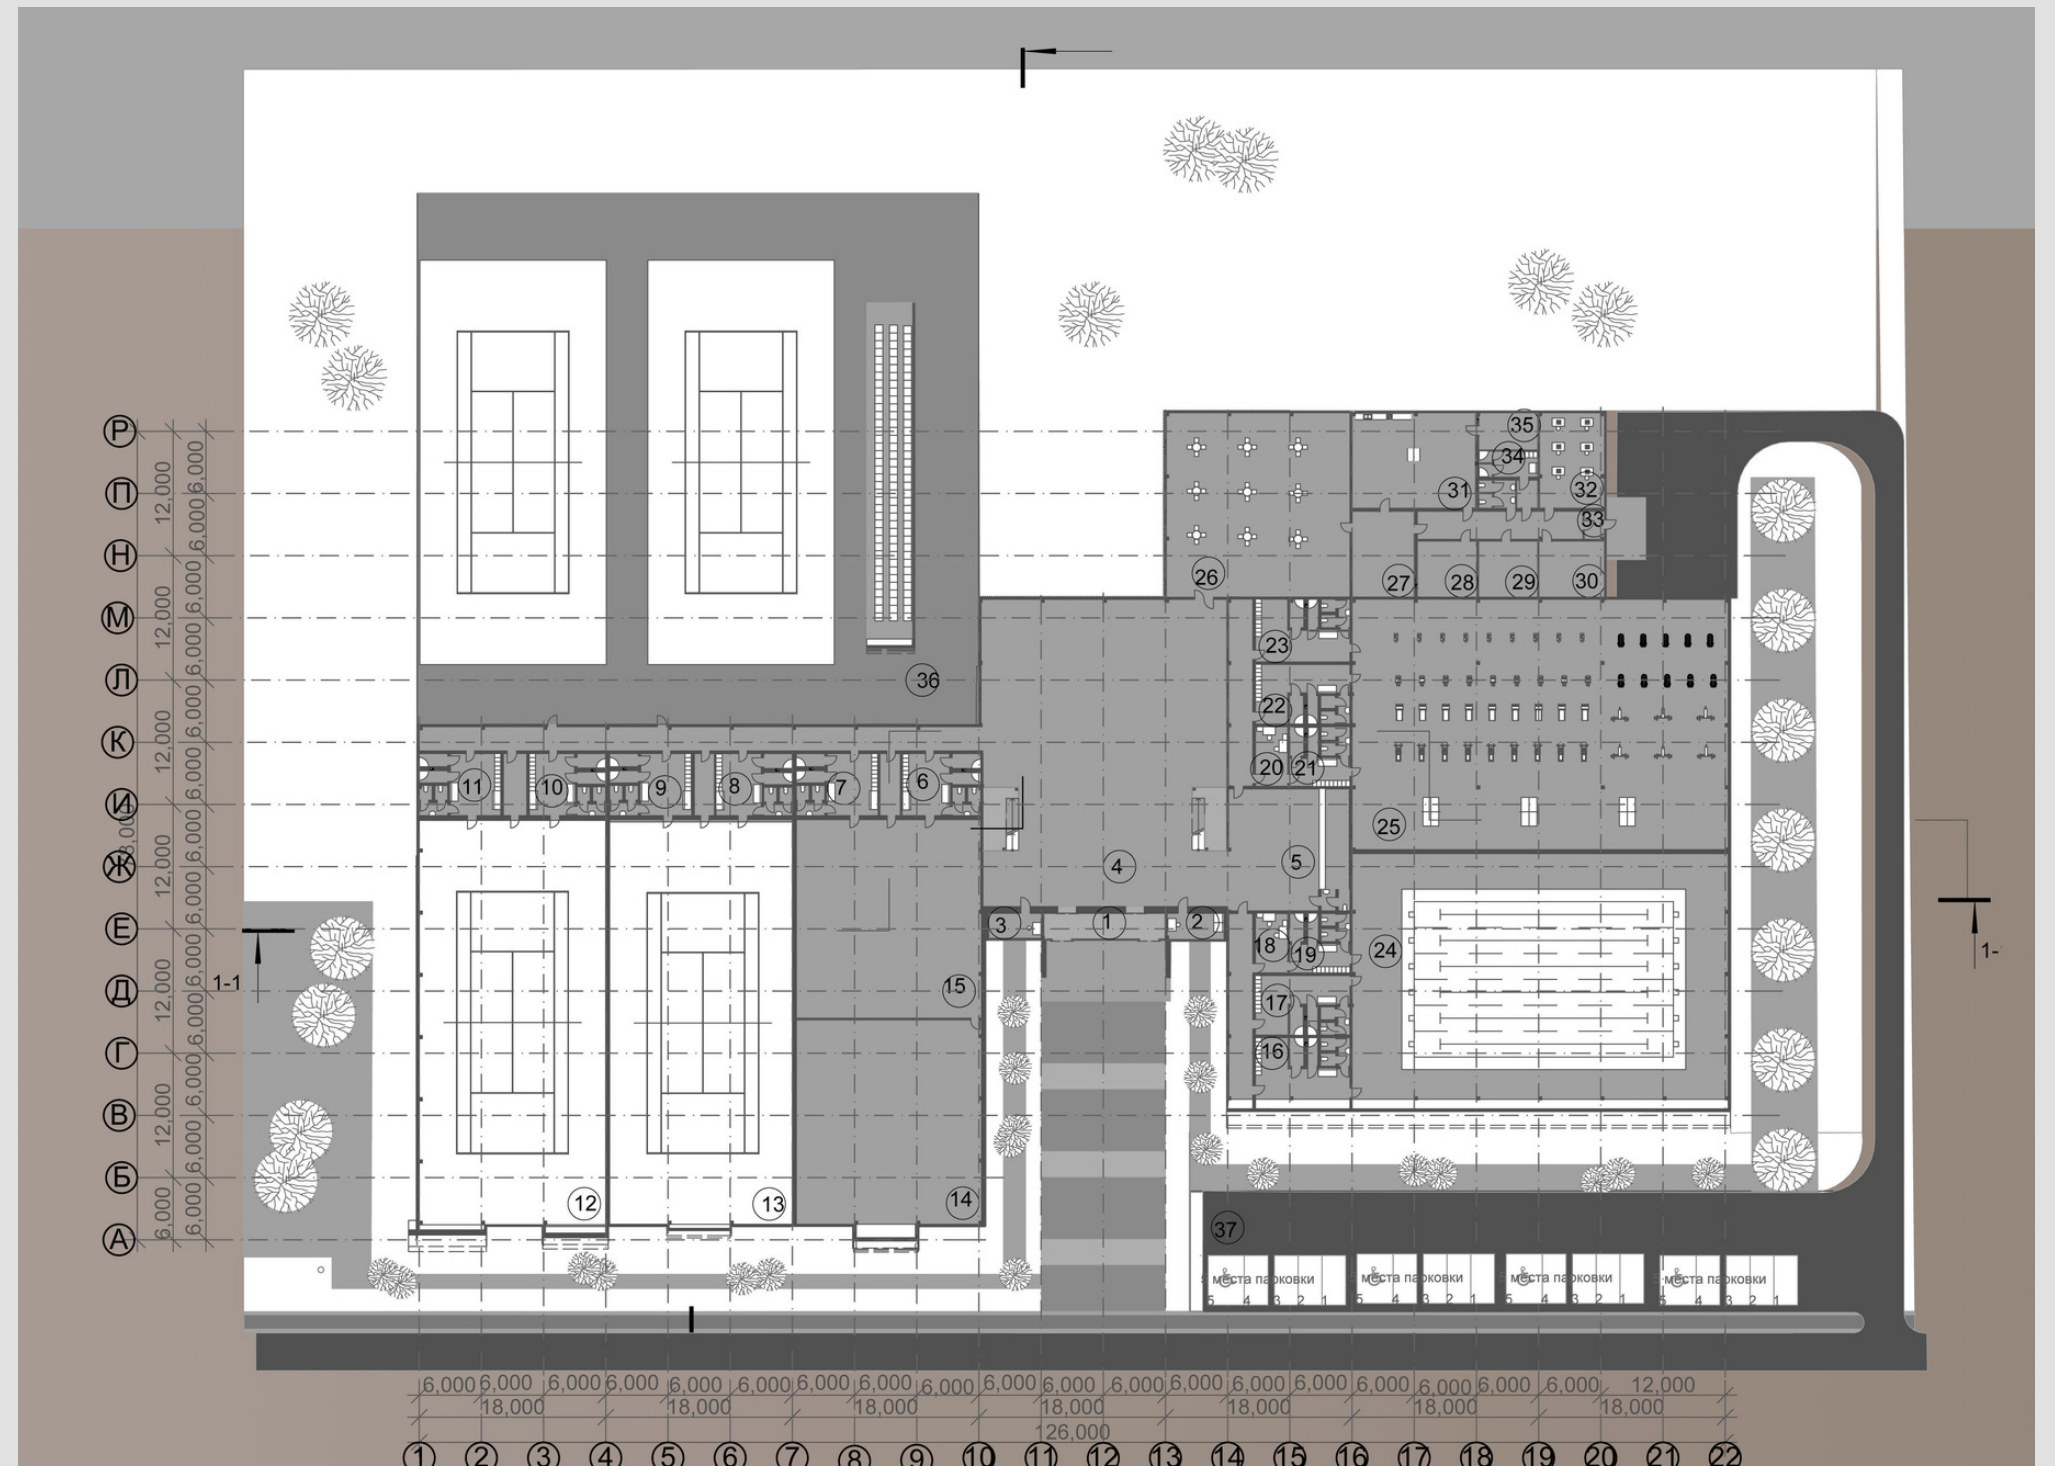

- | | | |
|---|---|--|
| 1. Vestibule – 30 m ² | 17., 22. Women's Changing Room – 38 m ² | 32. Admonostration office- 58 m ² |
| 2. Reception – 12 m ² | 18., 20. Coaches' Office – 20 m ² | 33. Tambour -5 m ² |
| 3. Security – 12 m ² | 19., 21. Coaches' Changing Room – 35 m ² | 34. Changing room- 10 m ² |
| 4. Lobby – 690 m ² | 24. Swimming Pool – 860 m ² | 35. Serving room -20 m ² |
| 5. Wardrobe – 60 m ² | 25. Gym – 880 m ² | 36. Outdoor tennis courts- 2800 m ² |
| 6., 8., 10. Men's Changing Room – 29 m ² | 26. Cafeteria Hall – 320 m ² | 37. Parking- 877 m ² |
| 7., 9., 11. Women's Changing Room – 29 m ² | 27. Dishwasher- 50 m ² | |
| 12., 13. Indoor tennis court – 820 m ² | 28., 29., 30. Storage-30 m ² | |
| 14., 15. Wall-to -wall game room-350 m ² | 31. Kitchen- 110 m ² | |
| 16., 23. Men's Changing Room – 38 m ² | 32. Admonostration office- 58 m ² | |

APARTMENT



Flat for 2 person				
BEDROOM	HALLWAY	BATHROOM	TOILET	
				
A serene and spacious retreat in soft tones of white, beige, and light gray. • A large bed with a geometric padded headboard that visually anchors the wall. • Symmetrical nightstands with lamps for balance and convenience. • Layered curtains (sheer and blackout) provide gentle natural light control.	• Clean and functional with subtle decorative touches. • Gray walls, light stone flooring with black tile accents. • Built-in storage units	The bathroom features glossy gray marble-effect tiles on both walls and floor, creating a clean and elegant backdrop. • Matte black fixtures — including the showerhead, faucet, and accessories — add contrast and a contemporary edge. • A floating white vanity with a full-width mirror enhances the sense of space and simplicity. • Minimalist black details throughout the room reinforce the modern aesthetic, resulting in a sleek and understated design.	Guest Toilet Designed in harmony with the main bathroom, this compact space features a clean and modern aesthetic. • Matte light gray marble-effect tiles cover the walls and floor, offering a calm and understated backdrop. • A feature wall with 3D geometric tiles adds texture and visual interest, creating a subtle focal point. • The layout includes a wall-mounted toilet, a recessed niche with decorative elements, and minimalist black fixtures that echo the apartment's overall design language.	

Flat for 2 person



- A built-in pantry is discreetly integrated into a niche located within the bay window zone.
- The kitchen includes a dining area and a relaxation corner within the bay window, featuring floor-to-ceiling windows and ambient lighting that casts a gentle glow in the evening, creating a cozy and inviting atmosphere.

A compact, modern kitchen designed to meet all functional needs while maintaining a clean, elegant aesthetic.

- Glossy handle-less cabinetry enhances the minimalist look, with reflective surfaces creating a subtle play of light.
- The backsplash features tiles in soft gray, beige, and muted pink tones, adding warmth and visual texture.
- The lower cabinets in beige harmonize beautifully with the backsplash palette.

This space is currently designed as a flexible area tailored to the needs of a young family.





- Conceived as a future children's room, it allows for easy transformation without major structural changes.
- The layout anticipates zones for sleeping, learning, and play, including elements for physical activity such as a climbing rope.
- The interior features a calm base palette with playful accents, easily adaptable to the child's age and preferences.
- Safe flooring, soft furnishings, and open shelving ensure comfort, practicality, and room for growth.

FOTO



SECONDARY SCHOOL



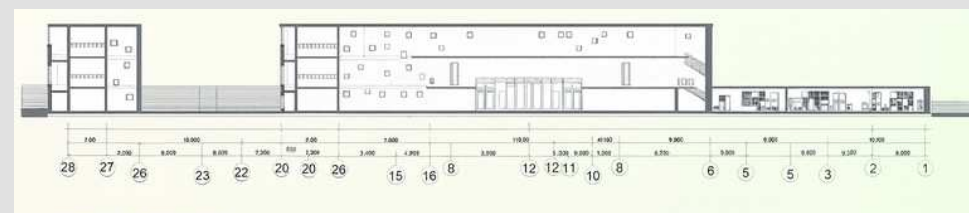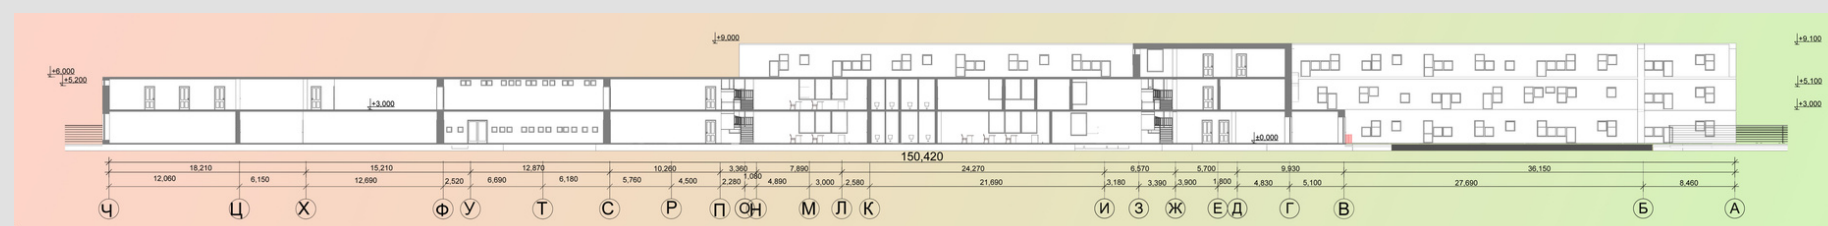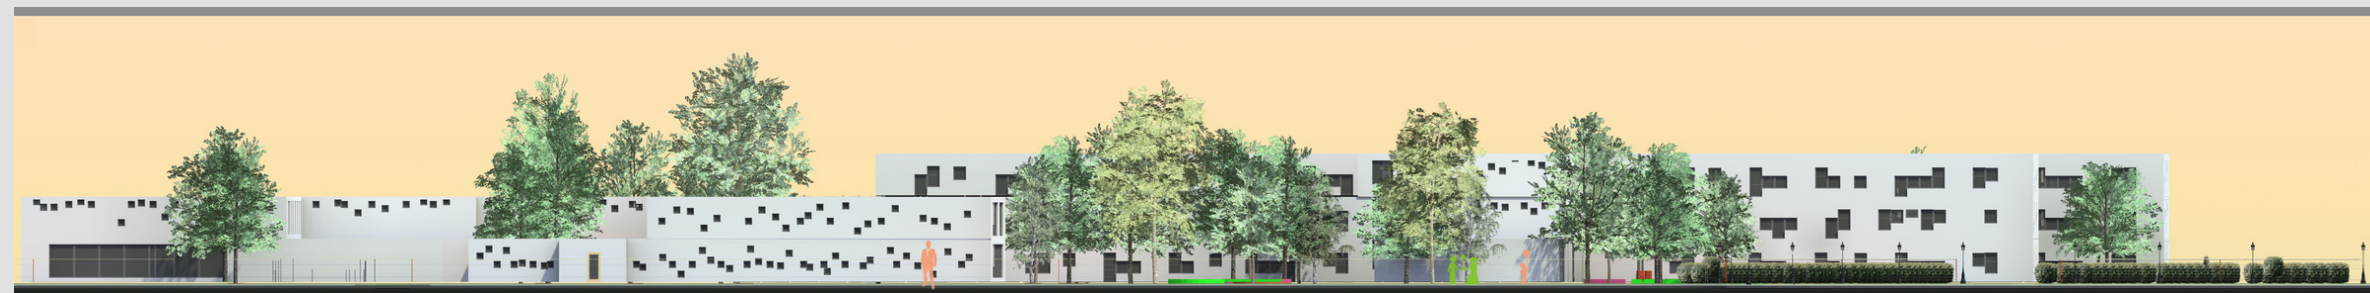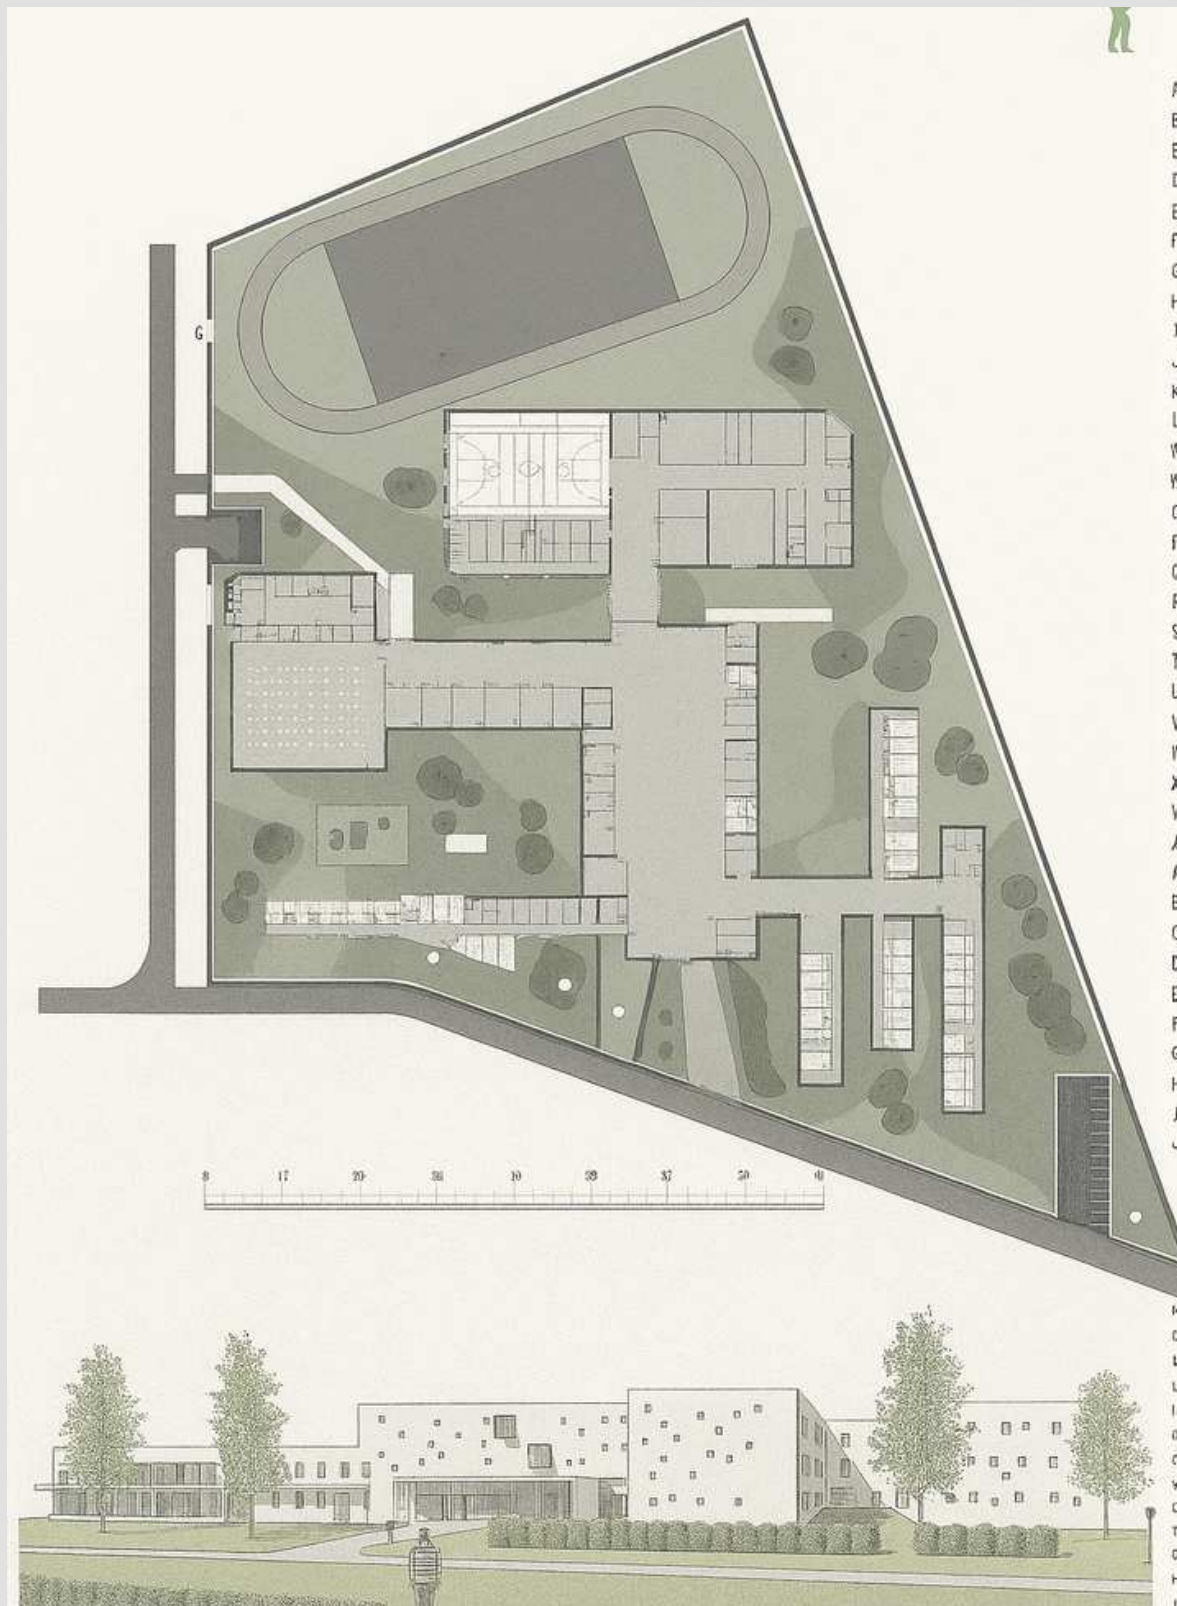

Architectural Concept and Functional Layout
 This school project is designed for a triangular site, responding to contemporary educational needs, safety standards, and the creation of a comfortable, child-friendly environment. The building is organized into clearly defined sections (A–J), allowing for effective zoning by age group and a phased learning process.

Comprehensive secondary school

The school includes all essential facilities: general classrooms, specialized subject rooms (chemistry, physics, IT), a library, cafeteria, administrative offices, restrooms, changing rooms, a sports hall, and outdoor activity areas. The entrance zone is emphasized with glass elements and bright accents, creating an open and welcoming atmosphere.

The facades are rendered in white with an irregular rhythm of black windows, adding visual dynamism and a modern character. Color accents are introduced on selected building sections and entrance doors, adding identity and orientation cues. Additionally, vibrant tones are used in the anti-trauma flooring of play and sports areas, enhancing safety and creating a cheerful atmosphere.

The landscape is fully integrated into the architecture: lawns, trees, benches, lanterns, and walkways form a cozy environment for rest and recreation. The sports zone is located at the top of the site and includes a running track and open play area.

This school is not just a functional building — it is a nurturing environment that shapes personality. The project provides:



- A safe, open space
- Visual transparency and accessibility
- Connection to nature
- Areas for learning, play, and relaxation
- Flexibility and adaptability to student needs

APARTAMENT





Kitchen + Loggia Extension:

The kitchen was expanded by integrating the loggia, allowing for a generous worktop and extended storage. This transformation created a spacious, light-filled culinary zone with clean lines and concealed lighting.

3-room apartment



This interior project was designed for a young family with two children, later adapted to accommodate a third child born during the design process. The apartment balances flexibility, functionality, and emotional warmth, with each zone tailored to evolving family needs.



- Entrance Hall:
- Equipped with built-in wardrobes for clothing storage, a large mirror to visually expand the space, and a floating shelf that appears weightless — adding a graphic, minimalist accent.
- Children’s Room:
- A spacious, adaptive zone with three sleeping areas, individual desks, storage units, and play space. A third bed was added without compromising ergonomics. The room includes active elements like a climbing wall, gym ladder, and a hanging bubble chair.

- Master Bedroom:
- Includes a built-in walk-in wardrobe clad in textured panels, forming a sculptural “cube” effect. Multiple lighting options enhance ambiance and highlight architectural details.
- Balcony Workspace:
- Transformed into a compact home office with underfloor heating — a quiet, light-filled retreat for focused work
- Living / Rest Area:
- A multifunctional space used for relaxation, dining, and hosting. It features layered lighting scenarios and is planned for future conversion into an additional children’s room.



Interior and landscape planning.



Sustainable and eco-friendly building solutions.



CHILDREN'S ART SCHOOL





ДИТЯЧА ШКОЛА МИСТЕЦТВ У МІСТІ КИЄВІ ПО ВУЛИЦІ АННІ АХМАТОВОЇ

